ALTERAÇÃO QUADRA-69

GLEBA 01 DA FAZENDA ÁGUA BRANCA

Propr.: Laerson Benedito Leonardi
João Sérgio Leonardi

GLEBA B-C

ALINHAMENTO		DIST.	AZIMUTE
10	11	29.03	97°50'49"
11	12	29.51	95°10'40"
12	13	27.52	87°50'24"
13	14	34.56	101°17'42"
14	15	40.50	79°31'37"
15	16	39.16	88°45'28"
16	17	37.26	111°55'22"
17	18	57.53	100°49'40"
18	19	37.65	93°51'35"
19	20	25.88	60°16'20"
20	21	31.08	82°55'48"
21	22	42.12	73°18'55"
22	23	190.72	90°01'48"
23	24	34.71	77°21'51"
24	25	43.40	99°36'45"
25	26	34.31	74°04'38"
26	27	13.22	25°54'08"
27	28	30.26	05°08'52"
28	29	72.76	69°27'21"
29	30	58.89	301°56'07"
30	31	29.96	28°51'30"
31	32	37.17	29°00'47"
32	33	21.26	11°38'43"
33	34	23.71	98°25'20"
34	35	17.35	65°31'18"
35	36	27.25	105°41'50"
36	37	32.76	116°31'33"
37	38	42.14	129°23'22"
38	39	19.72	124°43'33"
39	40	57.51	121°42'15"
40	41	68.41	124°17'01"
41	42	105.72	133°51'14"
42	43	47.32	122°44'03"
43	44	97.78	03°43'02"
44	45	66.10	65°37'03"
45	46	270.40	66°58'15"
46	47	6.31	103°21'08"
47	48	11,65	103°21'08"
48	49	30.64	103°21'08"
49	50	175.96	189°30'51"
50	51	172.92	108°26'36"
51	52	45.86	26°29'53"
52	53	27.01	41°09'42"
53	54	22.77	36°17'55"
54	55	39.16	350°50'04"
55	56	11.10	04°14'27"
56	57	147.40	79°54'22"
57	58	77.57	88°17'44"
58	59	11.35	15°15'58"
59	60	26.79	38°13'42"

GLEBA B-C (Contin.)

ALINHAMENTO		DIST.	AZIMUTE
60	61	11.96	25°47'07"
61	62	114.32	91°03'43"
62	63	36.52	78°19'07"
63	64	20.59	55°19'11"
64	65	116.78	48°43'39"
65	65A	214.85	72°56'40"
65A	66	75.70	72°56'40"
66	67	12.18	16°08'37"
67	68	212.72	74°33'46"
68	69	42.25	196°21'57"
69	70	43.85	189°18'58"
70	71	47.54	162°30'20"
71	72	23.94	173°03'38"
72	73	49.72	181°48'55"
73	74	50.67	191°44'37"
74	75	27.85	171°00'32"
75	76	19.01	154°26'51"
76	77	17.26	145°36'04"
77	78	23.71	133°46'05"
78	79	12.06	120°03'37"
79	80	12.52	102°50'51"
80	81	36.11	93°00'02"
81	82	75.50	101°31'49"
82	83	25.16	109°36'19"
83	84	49.54	125°18'22"
84	85	98.63	118°07'07"
85	86	50.72	124°39'28"
86	87	49.16	130°15'20"
87	88	85.20	135°32'29"
88	89	42.65	149°35'25"
89	90	57.13	149°38'58"
90	91	345.26	117°05'20"
91	260	105.22	112°12'24"
260	259	DC=25.77	em curva (r=28.00)
259	258	17.06	164°53'27"
258	257	DC=29.06	em curva (r=32.00)
257	256	120.30	112°51'21"
256	255	58.86	107°51'45"
255	254	DC=30.22	em curva (r=30.00)
254	253	21.16	50°08'15"
253	252	43.39	61°00'23"
252	102	3.86	84°46'02"
102	103	10.33	201°39'11"
103	104	79.02	206°11'46"
104	105	78.53	202°01'51"
105	106	75.23	197°06'12"
106	107	42.85	199°19'03"
107	108	117.02	186°55'20"
108	109	20.85	207°55'10"
109	110	23.30	221°55'15"

GLEBA B-C (Contin.)

ALINHAMENTO		DIST.	AZIMUTE
110	111	129.06	237°12'38"
111	112	80.88	250°12'48"
112	113	27.56	234°53'48"
113	114	81.57	233°06'43"
114	115	89.92	235°22'36"
115	116	148.46	228°41'47"
116	117	18.81	219°53'07"
117	118	21.12	211°12'54"
118	119	27.56	202°18'02"
119	120	43.48	216°10'23"
120	121	91.26	203°18'59"
121	122	97.60	197°10'19"
122	123	72.07	201°32'46"
123	124	168.80	229°01'06"
124	125	77.48	225°58'01"
125	126	98.37	231°57'31"
126	127	29.26	215°59'31"
127	128	102.00	277°23'23"
128	129	136.09	265°50'51"
129	130	76.27	276°22'18"
130	131	62.24	288°32'08"
131	132	67.37	300°38'35"
132	133	79.15	286°13'49"
133	134	88.71	278°08'40"
134	135	30.32	277°10'27"
135	136	41.23	271°48'40"
136	137	18.83	263°29'45"
137	138	27.91	257°46'41"
138	139	45.67	256°23'29"
139	140	23.71	270°13'12"
140	141	38.60	259°37'55"
141	142	64.53	268°08'03"
142	143	23.11	286°54'32"
143	144	28.63	268°24'09"
144	145	82.38	279°22'53"
145	146	11.37	297°14'28"
146	147	14.12	269°25'11"
147	148	40.78	280°15'17"
148	149	20.95	290°43'50"
149	150	4.69	283°49'00"
150	151	26.65	282°41'49"
151	152	9.92	276°02'34"
152	153	7.53	303°42'40"
153	154	56.64	320°26'02"
154	155	112.32	302°04'02"
155	156	39.41	30°45'33"
156	157	34.98	33°50'47"
157	158	26.67	45°11'29"
158	159	21.63	31°32'50"
159	160	33.95	26°16'47"

GLEBA B-C (Contin.)

ALINHAMENTO		DIST.	AZIMUTE
160	161	21.11	13°02'16"
161	162	36.42	06°50'06"
162	163	6.05	00°34'40"
163	164	33.15	01°31'41"
164	165	33.35	11°15'51"
165	166	90.45	19°53'09"
166	167	11,11	304°29'25"
167	168	99,67	304°06'52"
168	169	67.94	305°59'30"
169	170	39.87	304°48'25"
170	171	95.37	297°30'23"
171	172	286.91	296°54'57"
172	173	64.07	293°54'23"
173	174	89.29	291°33'44"
174	175	47.00	309°09'45"
175	176	19.85	294°12'41"
176	177	6.13	277°44'15"
177	178	31.31	290°51'57"
178	179	26.25	298°58'02"
179	180	44.77	304°30'11"
180	181	27.73	294°00'23"
181	182	11.87	275°29'02"
182	183	11.12	266°13'49"
183	184	43.31	250°04'32"
184	185	27.95	295°18'22"
185	186	61.05	291°04'11"
186	187	50.09	286°34'41"
187	188	213.75	290°01'35"
188	189	67.79	290°39'42"
189	190	54.72	289°05'25"
190	191	38.35	289°14'34"
191	192	261.00	290°29'31"
192	204	DC=112.05	em curva (r=510.00)
204	203	147.00	355°51'31"
203	202	DC=166.51	em curva (r=270.00)
202	201	67.15	319°09'53"
201	200	DC=106.98	em curva (r=150.00)
200	10	26.02	00°01'39"

(Quadras/Lotes)			(Quadras/Lotes)		
DESCR.	ÁREA (m²)	N° DE LOTES	DESCR.	ÁREA (m²)	N° DE LOTES
QUADRA - 1	14.159,72	7	QUADRA - 63	20.661,63	10
QUADRA - 2	31.187,79	15	QUADRA - 64	37.540,26	17
QUADRA - 3	7.248,97	3	QUADRA - 65	34.481,24	15
QUADRA - 4	14.749,97	7	QUADRA - 66	25.693,91	11
QUADRA - 5	13.698,00	6	QUADRA - 67	28.011,75	13
QUADRA - 6	44.787,29	19	QUADRA - 68	40.230,44	18
QUADRA - 7	37.921,81	18	QUADRA - 69	19.569,59	9
QUADRA - 8	33.567,21	16	QUADRA - 70	12.471,66	6
QUADRA - 9	4.022,92	2	QUADRA - 71	18.829,74	9
QUADRA - 10	14.994,81	6	QUADRA - 72	4.118,98	2
QUADRA - 11	9.739,23	4	QUADRA - 73	8.663,19	4
QUADRA - 12	14.493,77	6	QUADRA - 74	3.708,89	1
QUADRA - 13	15.189,90	7	QUADRA - 75	16.429,27	7
QUADRA - 14	18.927,98	7	QUADRA - 76	10.125,41	5
QUADRA - 15	15.097,64	7	QUADRA - 77	10.800,00	5
QUADRA - 16	11.724,55	5	QUADRA - 78	21.795,87	10
QUADRA - 17	17.072,19	7	QUADRA - 79	8.915,78	4
QUADRA - 18	21.099,66	9	QUADRA - 80	15.034,48	7
QUADRA - 19	10.054,69	5	QUADRA - 81	22.951,13	10
QUADRA - 20	12.347,65	6	QUADRA - 82	16.093,42	7
QUADRA - 21	20.721,53	9	QUADRA - 83	17.324,85	7
QUADRA - 22	36.032,61	16	QUADRA - 84	11.765,54	5
QUADRA - 23	36.291,83	16	QUADRA - 85	24.950,66	9
QUADRA - 24	35.844,30	15	QUADRA - 86	32.553,25	13
QUADRA - 25	18.291,79	7	QUADRA - 87	29.458,46	13
QUADRA - 26	7.829,50	3	QUADRA - 88	35.797,96	15
QUADRA - 27	12.573,91	5	QUADRA - 89	42.118,15	19
QUADRA - 28	13.542,55	5	QUADRA - 90	13.442,20	6
QUADRA - 29	7.236,69	2	QUADRA - 91	30.064,35	13
QUADRA - 30	10.894,96	4	QUADRA - 92	8.520,00	4
QUADRA - 31	30.737,49	11	QUADRA - 93	19.590,37	9
QUADRA - 32	19.136,85	8	QUADRA - 94	28.632,26	13
QUADRA - 33	36.326,49	16	QUADRA - 95	15.782,56	7
QUADRA - 34	5.434,71	2	QUADRA - 96	34.782,77	15
QUADRA - 35	12.213,05	5	QUADRA - 97	30.393,14	13
QUADRA - 36	16.435,16	7	QUADRA - 98	45.404,43	20
QUADRA - 37	31.171,68	14	QUADRA - 99	4.305,21	2
QUADRA - 38	31.217,53	15	QUADRA - 100	9.382,81	4
QUADRA - 39	27.785,20	13	QUADRA - 101	14.260,82	6
QUADRA - 40	21.949,81	10	QUADRA - 102	2.744,23	1
QUADRA - 41	13.089,86	6	QUADRA - 103	24.910,47	10
QUADRA - 42	40.712,80	19	QUADRA - 104	11.085,81	5
QUADRA - 43	31.042,76	15	QUADRA - 105	22.533,09	10
QUADRA - 44	17.083,66	8	QUADRA - 106	10.580,21	4
QUADRA - 45	23.710,53	11	QUADRA - 107	12.291,42	5
QUADRA - 46	32.657,10	16	QUADRA - 108	27.914,24	11
QUADRA - 47	17.673,85	8	QUADRA - 109	19.825,01	9
QUADRA - 48	39.034,56	16	QUADRA - 110	12.880,37	6
QUADRA - 49	40.931,99	19	QUADRA - 111	45.243,48	20
QUADRA - 50	21.645,07	9	QUADRA - 112	38.928,32	18
QUADRA - 51	21.494,64	9	QUADRA - 113	32.923,45	15
QUADRA - 52	34.510,83	14	QUADRA - 114	34.859,53	16
QUADRA - 53	18.926,87	8	QUADRA - 115	37.373,18	17
QUADRA - 54	19.120,37	9	QUADRA - 116	4.595,78	2
QUADRA - 55	10.865,49	5	QUADRA - 117	17.228,05	6
QUADRA - 56	12.269,67	6	QUADRA - 118	23.480,77	9
QUADRA - 57	12.280,17	6	QUADRA - 119	15.494,99	6
QUADRA - 58	12.316,18	6	QUADRA - 120	18.577,70	6
QUADRA - 59	18.329,42	9	QUADRA - 121	29.002,52	9
QUADRA - 60	15.909,64	6	QUADRA - 122	15.356,88	7
QUADRA - 61	32.632,85	14	QUADRA - 123	25.301,65	11
QUADRA - 62	26.068,47	12			
			TOTAL GERAL	2.613.847,75	1.142

SISTEMA VIÁRIO			
DESCR.	ÁREA (m²)	DESCR.	ÁREA (m²)
AV-01	9.381,28	VIELA-01	226,50
AV-02	20.832,00	VIELA-02	310,89
RUA 1	2.826,37	VIELA-03	61,53
RUA 2	7.136,75	VIELA-04	231,13
RUA 3	6.442,40	VIELA-05	221,79
RUA 4	8.507,24	VIELA-06	201,64
RUA 5	4.467,75	VIELA-07	59,66
RUA 6	7.542,96	VIELA-08	213,71
RUA 7	5.280,84	VIELA-09	190,18
RUA 8	8.770,49	VIELA-10	163,10
RUA 9	13.000,48	VIELA-11	351,85
RUA 10	3.261,09	VIELA-12	379,70
RUA 11	3.905,86	VIELA-13	308,83
RUA 12	8.155,07	VIELA-14	235,11
RUA 13	5.069,14	VIELA-15	290,99
RUA 14	23.984,75	VIELA-16	222,52
RUA 15	2.649,34	VIELA-17	240,00
RUA 16	21.295,39	VIELA-18	480,00
RUA 17	2.008,96	VIELA-19	480,00
RUA 18	2.019,29	VIELA-20	480,00
RUA 19	3.331,16	VIELA-21	476,26
RUA 20	5.541,94	VIELA-22	283,41
RUA 21	8.053,34	VIELA-23	514,50
RUA 22	16.264,06	VIELA-24	657,32
RUA 23	9.006,80	VIELA-25	240,12
RUA 24	2.827,43	VIELA-26	240,00
RUA 25	8.603,78	VIELA-27	215,88
RUA 26	26.331,73	VIELA-28	480,01
RUA 27	10.177,22	VIELA-29	480,00
RUA 28	10.426,16	VIELA-30	508,00
RUA 29	7.184,79	VIELA-31	240,00
RUA 30	2.021,22	VIELA-32	294,61
RUA 31	2.021,40	VIELA-33	240,00
RUA 32	4.124,32	VIELA-34	480,00
RUA 33	3.390,60	VIELA-35	240,00
RUA 34	2.827,43	VIELA-36	240,00
RUA 35	5.110,73	VIELA-37	240,05
RUA 36	3.254,69	VIELA-38	480,00
RUA 37	14.641,04	VIELA-39	242,38
RUA 38	4.366,44	VIELA-40	220,00
RUA 39	16.540,14	VIELA-41	318,27
RUA 40	5.911,85	VIELA-42	266,00
RUA 41	7.643,67	VIELA-43	240,00
RUA 42	2.827,43	VIELA-44	460,00
RUA 43	4.986,44	VIELA-45	299,44
RUA 44	9.697,61	VIELA-46	292,29
RUA 45	12.733,11	VIELA-47	64,86
RUA 46	4.606,59	VIELA-48	380,01
RUA 47	7.983,51	VIELA-49	450,99
RUA 48	2.827,43	VIELA-50	220,11
RUA 49	1.604,95		
RUA 50	13.146,54		
RUA 51	23.819,34		
RUA 52	8.929,65		
RUA 53	2.010,70		
RUA 54-A	7.403,84		
RUA 54-B	3.343,23		
RUA 54-C	8.510,73		
RUA 55	36.576,19		
RUA 56	9.264,74		
RUA 57	2.006,00		
RUA 58	1.134,11		
RUA 59	2.415,54		
RUA 60	5.343,39		
SUB-TOTAL	517.310,46	SUB-TOTAL	15.353,64
		TOTAL GERAL	532.664,10

ÁREA INSTITUCIONAL	
DESCR.	ÁREA (m²)
A.I. - 01	56.496,54
A.I. - 02	80.957,26
A.I. - 03	98.727,93
TOTAL GERAL	236.181,73

ÁREA VERDE	
DESCR.	ÁREA (m²)
A.V.- 01	127.981,93
A.V.- 02	42.439,52
A.V.- 03	186.342,26
A.V.- 04	3.492,51
A.V.- 05	221.932,13
A.V.- 06	70.712,02
A.V.- 07	104.328,70
A.V.- 08	84.520,91
A.V.- 09	103.864,94
A.V.- 10	105.898,00
A.V.- 11	4.446,42
A.V.- 12	77.604,63
A.V.- 13	84.929,01
A.V.- 14	11.837,72
A.V.- 15	6.947,02
TOTAL GERAL	1.237.277,72

ÁREA RESERVADA	
DESCR.	ÁREA (m²)
A.R. - 01	55.491,75
A.R. - 02	2.509,92
A.R. - 03	8.845,32
A.R. - 04	2.827,43
A.R. - 05	13.035,06
TOTAL GERAL	82.709,48

ÁREA DESTINADA À EQUIPAMENTO URBANO	
DESCR.	ÁREA (m²)
A.D.E.U. - 01	361,36
A.D.E.U. - 02	377,46
A.D.E.U. - 03	399,08
A.D.E.U. - 04	384,85
A.D.E.U. - 05	364,29
A.D.E.U. - 06	407,07
A.D.E.U. - 07	372,29
A.D.E.U. - 08	383,08
A.D.E.U. - 09	443,19
A.D.E.U. - 10	418,20
A.D.E.U. - 11	660,00
A.D.E.U. - 12	579,56
A.D.E.U. - 13	954,38
A.D.E.U. - 14	388,69
A.D.E.U. - 15	1.361,94
A.D.E.U. - 16	674,08
TOTAL GERAL	8.529,52

PERFIL TRANSVERSAL DE RUAS

ESCALA 1:200

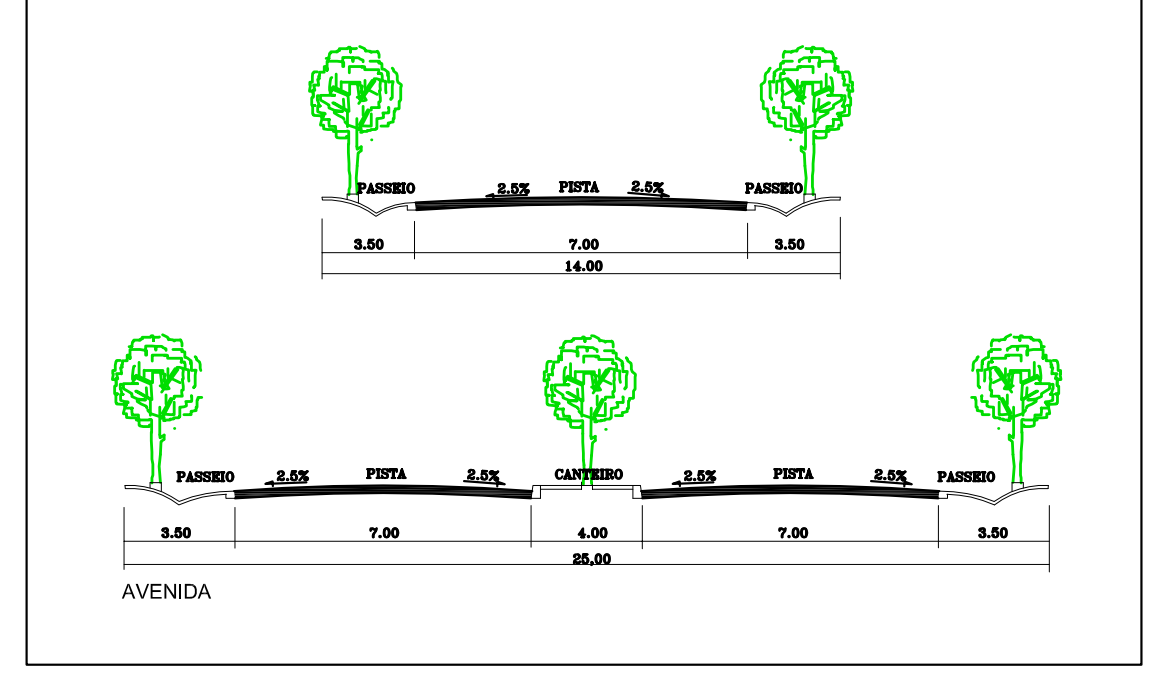

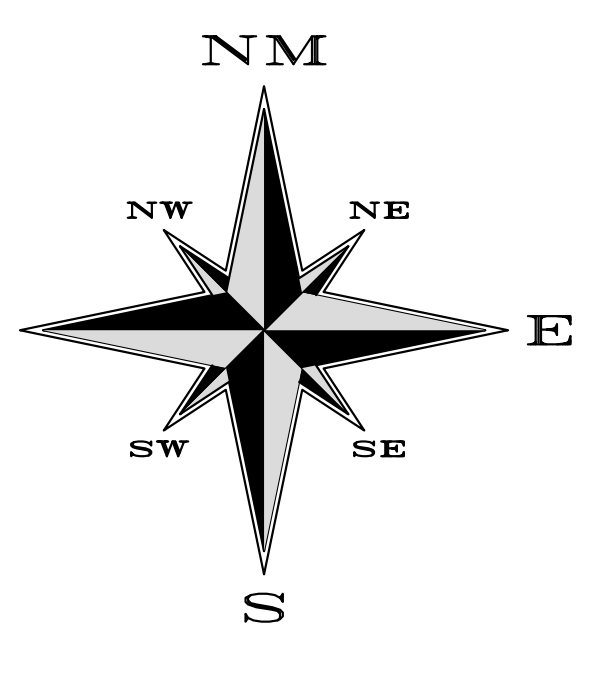

OBS.:

Estaqueamento a cada 20,00m ______ Vide Projeto Geométrico - Folha 3/8
Faixas não edificáveis nos lotes ______ Vide Projeto do Sistema de Esgoto - Folha 7/8
Sentido do escoamento das águas ______ Vide Projeto de Terraplenagem - Folha 4/8

PROJETO URBANÍSTICO

FOLHA
1/8

LOTEAMENTO RESIDENCIAL

DENOMINAÇÃO
PARQUE TERRAS DE SANTA CECÍLIA

BAIRRO
PINHEIRINHO

MUNICÍPIO
ITU - SP

PROPR.
SANTA CECÍLIA AGROPECUÁRIA E PARTICIPAÇÕES LTDA.
SENPAR - TERRAS DE S.JOSÉ EMPREEND. TURÍSTICOS LTDA.

SITUAÇÃO SEM ESCALA

VIDE AO LADO

SANTA CECÍLIA AGROPECUÁRIA E PARTICIPAÇÕES LTDA.

SENPAR - TERRAS DE S.JOSÉ EMPREEND.TURÍSTICOS LTDA.

QUADRO DE ÁREAS	ÁREA	TAXA
- ÁREAS DE LOTES (1142 unid.)	2.613.847,75 m²	55,34 %
- ÁREAS PÚBLICAS		
SISTEMA VIÁRIO	532.664,10 m²	11,27 %
ÁREA P/ AMPL.DA ITU-138	12.241,69 m²	0,26 %
ÁREA INSTITUCIONAL	236.181,73 m²	5,00 %
ÁREA DEST.EQUIP.URBANO	8.529,52 m²	0,18 %
ESPAÇOS LIVRES DE USO PUBLICO		
ÁREAS VERDES	866.146,15 m²	18,34 %
SISTEMAS DE LAZER	371.131,57 m²	7,86 %
- OUTROS		
ÁREA RESERVADA	82.709,48 m²	1,75 %
- ÁREA TOTAL DA GLEBA	4.723.451,99 m²	100,00 %

RESPONSÁVEL TÉCNICO
VITOR ROGERIO FEDERMANN
Engenheiro Civil CREA 0600593516
Inscr.Munic.: 4429
ART nº 92221220020063027

OBS.: O presente projeto está vinculado ao processo n°2266/02 da Prefeitura da Estância Turística de Itu

data	revisão	escala
23/10/2014	11/2005-04	1:3000

SITUAÇÃO SEM ESCALA